

GHI CHÚ
Toàn bộ kích thước trong hồ sơ là kích thước hoàn thiện.
Kiểm tra lại kích thước thực tế trước khi thi công.
Kết hợp các bản vẽ kiến trúc, kết cấu, điện, nước để thi công.
Phải thực hiện đầy đủ những chỉ dẫn kỹ thuật trong bản vẽ.
Không thay đổi bản vẽ dưới mọi hình thức nếu không được sự chấp thuận của đơn vị thiết kế.
© COPYRIGHT 2016

NGÀY	LẦN	NỘI DUNG SỬA ĐỔI
.../.../...	1	
.../.../...	2	
.../.../...	3	

DỰ ÁN :
.....

ĐỊA ĐIỂM: .....
.....

CHỦ ĐẦU TƯ :
.....

ĐỊA CHỈ : .....
.....
TEL: .....


I.D ARCHITECTURE AND FURNITURE
ĐỊA CHỈ: SỐ 74A/116 NHÂN HÒA, NHÂN CHÍNH, HÀ NỘI
TEL: 04 22 84 66 99
WEBSITE: HTTP://IDSTUDIO.VN

CHỦ TRÌ DỰ ÁN	THIẾT KẾ CHÍNH	NGƯỜI VẼ	KIỂM

TÊN BẢN VẼ

MẶT BẰNG TỔNG THỂ

NGÀY:.....
TỶ LỆ: 1/100
HIỆU CHỈNH 00
BẢN VẼ KT-

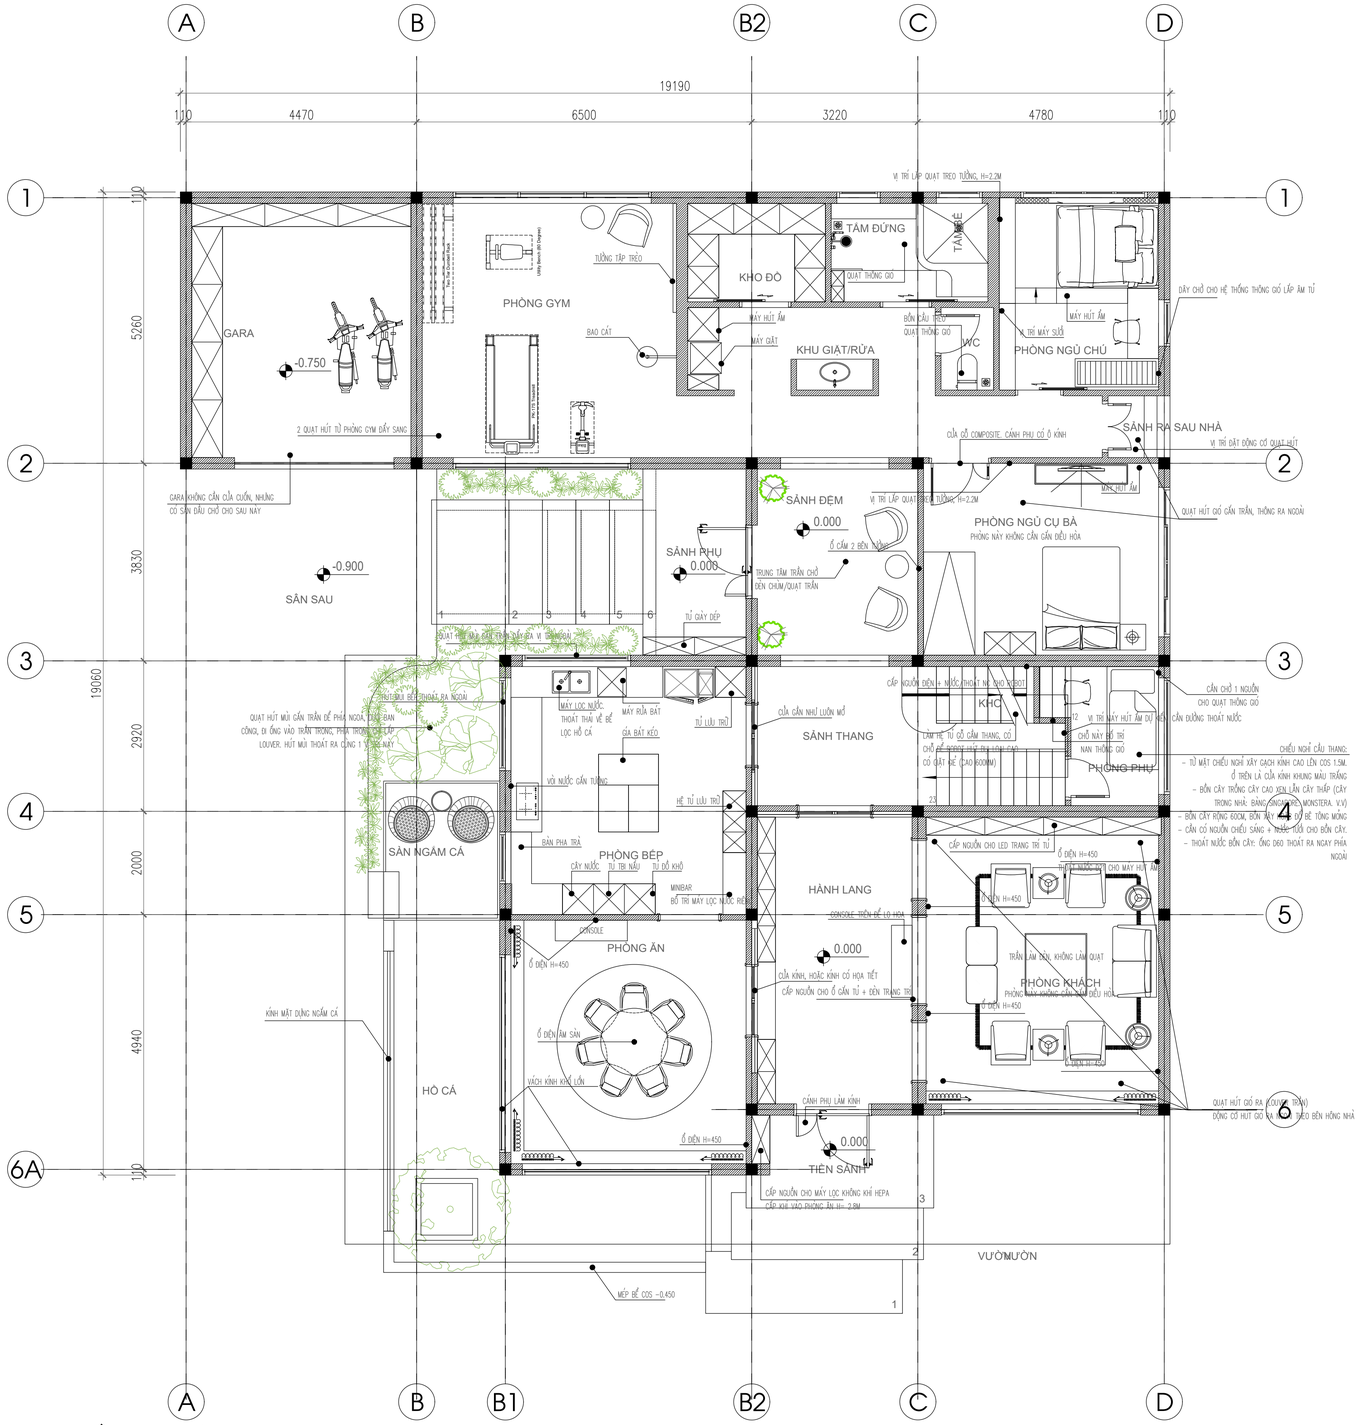

MẶT BẰNG TẦNG 1

MB ...

1:100

GHI CHÚ

Toàn bộ kích thước trong hồ sơ là kích thước hoàn thiện.
Kiểm tra lại kích thước thực tế trước khi thi công.
Kết hợp các bản vẽ kiến trúc, kết cấu, điện, nước để thi công.
Phải thực hiện đầy đủ những chỉ dẫn kỹ thuật trong bản vẽ.
Không thay đổi bản vẽ dưới mọi hình thức nếu không được sự chấp thuận của đơn vị thiết kế.

© COPYRIGHT 2016

NGÀY	LẦN	NỘI DUNG SỬA ĐỔI
.../.../...	1	
.../.../...	2	
.../.../...	3	

DỰ ÁN : .....

ĐỊA ĐIỂM: .....

CHỦ ĐẦU TƯ : .....

ĐỊA CHỈ : .....

TEL: .....

I.D ARCHITECTURE AND FURNITURE
ĐỊA CHỈ: SỐ 74A/116 NHÂN HÒA, NHÂN CHÍNH, HÀ NỘI
TEL: 04 22 84 66 99
WEBSITE: HTTP://IDSTUDIO.VN

CHỦ TRÌ DỰ ÁN	THIẾT KẾ CHÍNH	NGƯỜI VẼ	KIỂM

TÊN BẢN VẼ


PHƯƠNG ÁN SƠ BỘ

NGÀY:.....

TỶ LỆ: 1/100

HIỆU CHỈNH 00

BẢN VẼ KT-

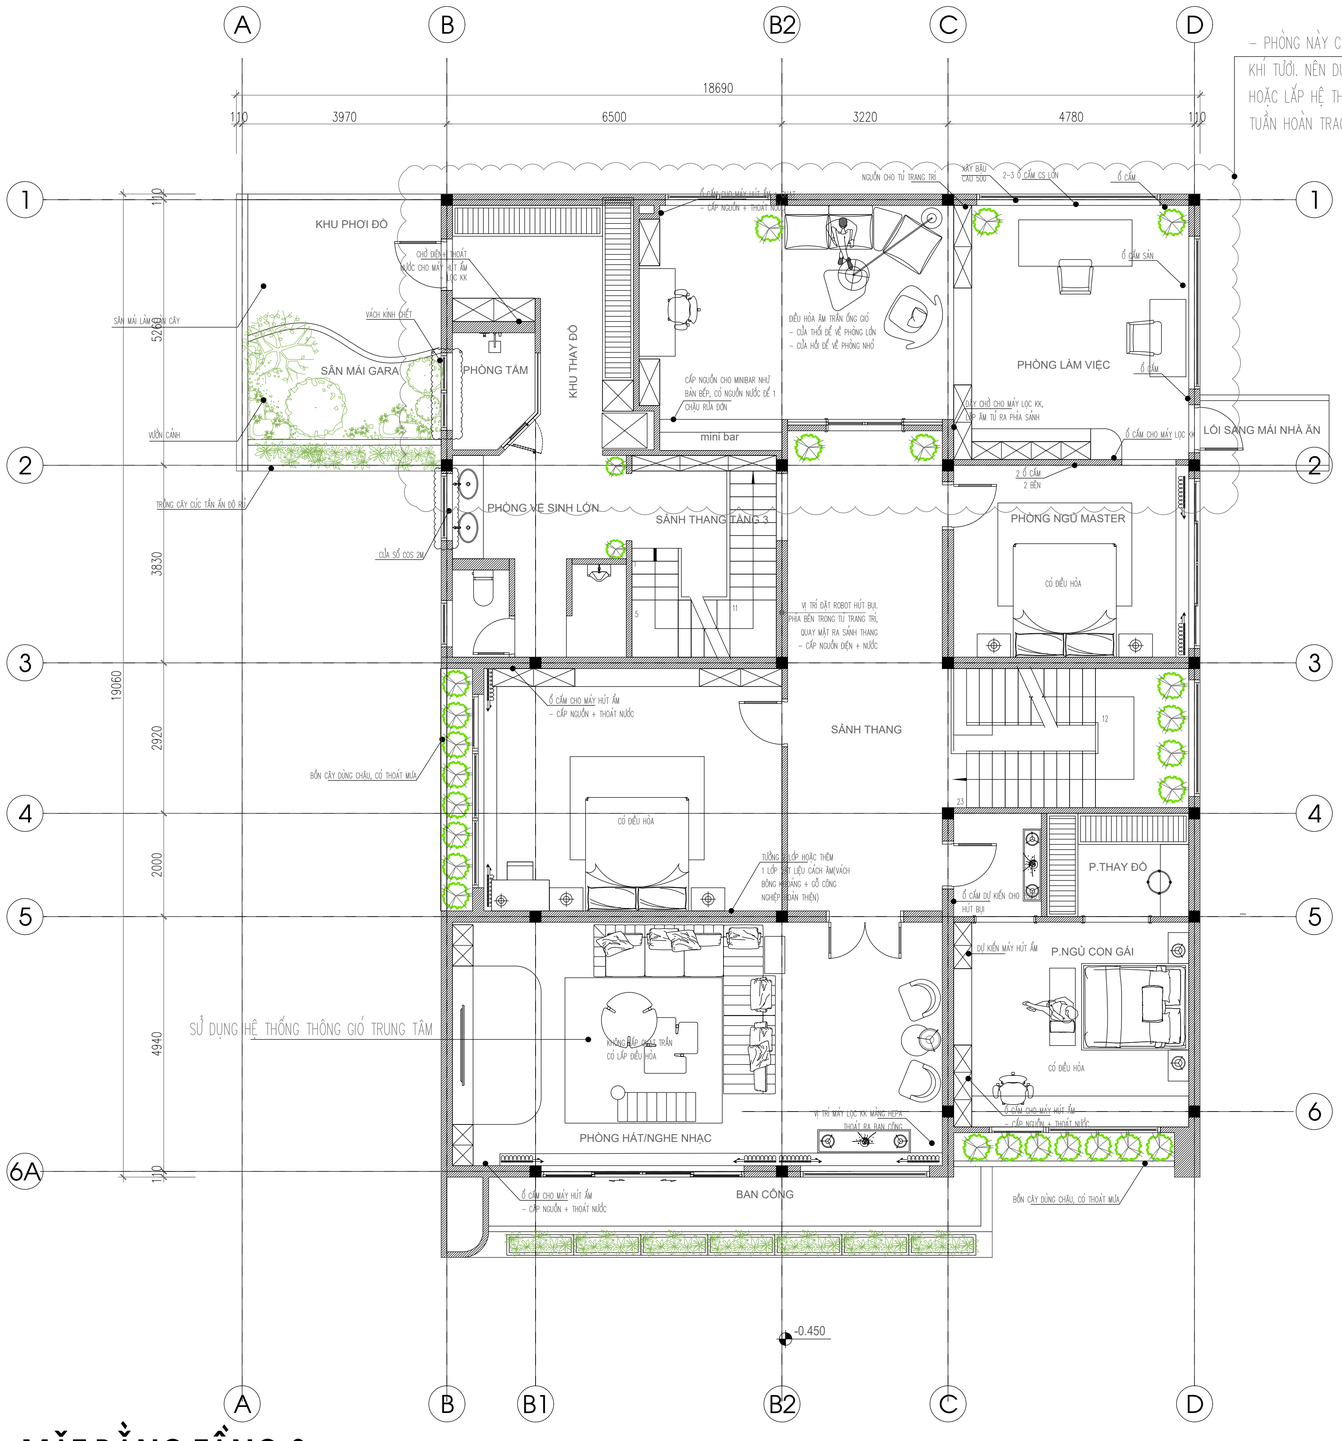

– PHÒNG NÀY CẦN XEM LẠI HỆ THỐNG THÔNG GIÓ CẤP KHÍ TƯƠI. NÊN DÙNG HỆ ÂM TRẦN ĐỂ ĐẢM BẢO THẨM MỸ. HOẶC LẮP HỆ THỐNG ĐIỀU HÒA THÔNG GIÓ CẤP KHÍ TƯƠI TUẦN HOÀN TRAO ĐỔI NHIỆT CỦA DAIKIN LUÔN.

MB
...

MẶT BẰNG TẦNG 2

1:100

GHI CHÚ
Toàn bộ kích thước trong hồ sơ là kích thước hoàn thiện.
Kiểm tra lại kích thước thực tế trước khi thi công.
Kết hợp các bản vẽ kiến trúc, kết cấu, điện, nước để thi công.
Phải thực hiện đầy đủ những chỉ dẫn kỹ thuật trong bản vẽ.
Không thay đổi bản vẽ dưới mọi hình thức nếu không được sự chấp thuận của đơn vị thiết kế.
© COPYRIGHT 2016

NGÀY	LẦN	NỘI DUNG SỬA ĐỔI
.../.../...	1	
.../.../...	2	
.../.../...	3	

DỰ ÁN :
.....
ĐỊA ĐIỂM: .....
.....


CHỦ ĐẦU TƯ :
.....
ĐỊA CHỈ : .....
.....
TEL: .....

I.D ARCHITECTURE AND FURNITURE
ĐỊA CHỈ: SỐ 74A/116 NHÂN HÒA, NHÂN CHÍNH, HÀ NỘI
TEL: 04 22 84 66 99
WEBSITE: HTTP://IDSTUDIO.VN

CHỦ TRÌ DỰ ÁN	THIẾT KẾ CHÍNH	NGƯỜI VẼ	KIỂM

TÊN BẢN VẼ
PHƯƠNG ÁN SƠ BỘ

NGÀY:.....
TỶ LỆ: 1/100
HIỆU CHỈNH 00
BẢN VẼ KT-

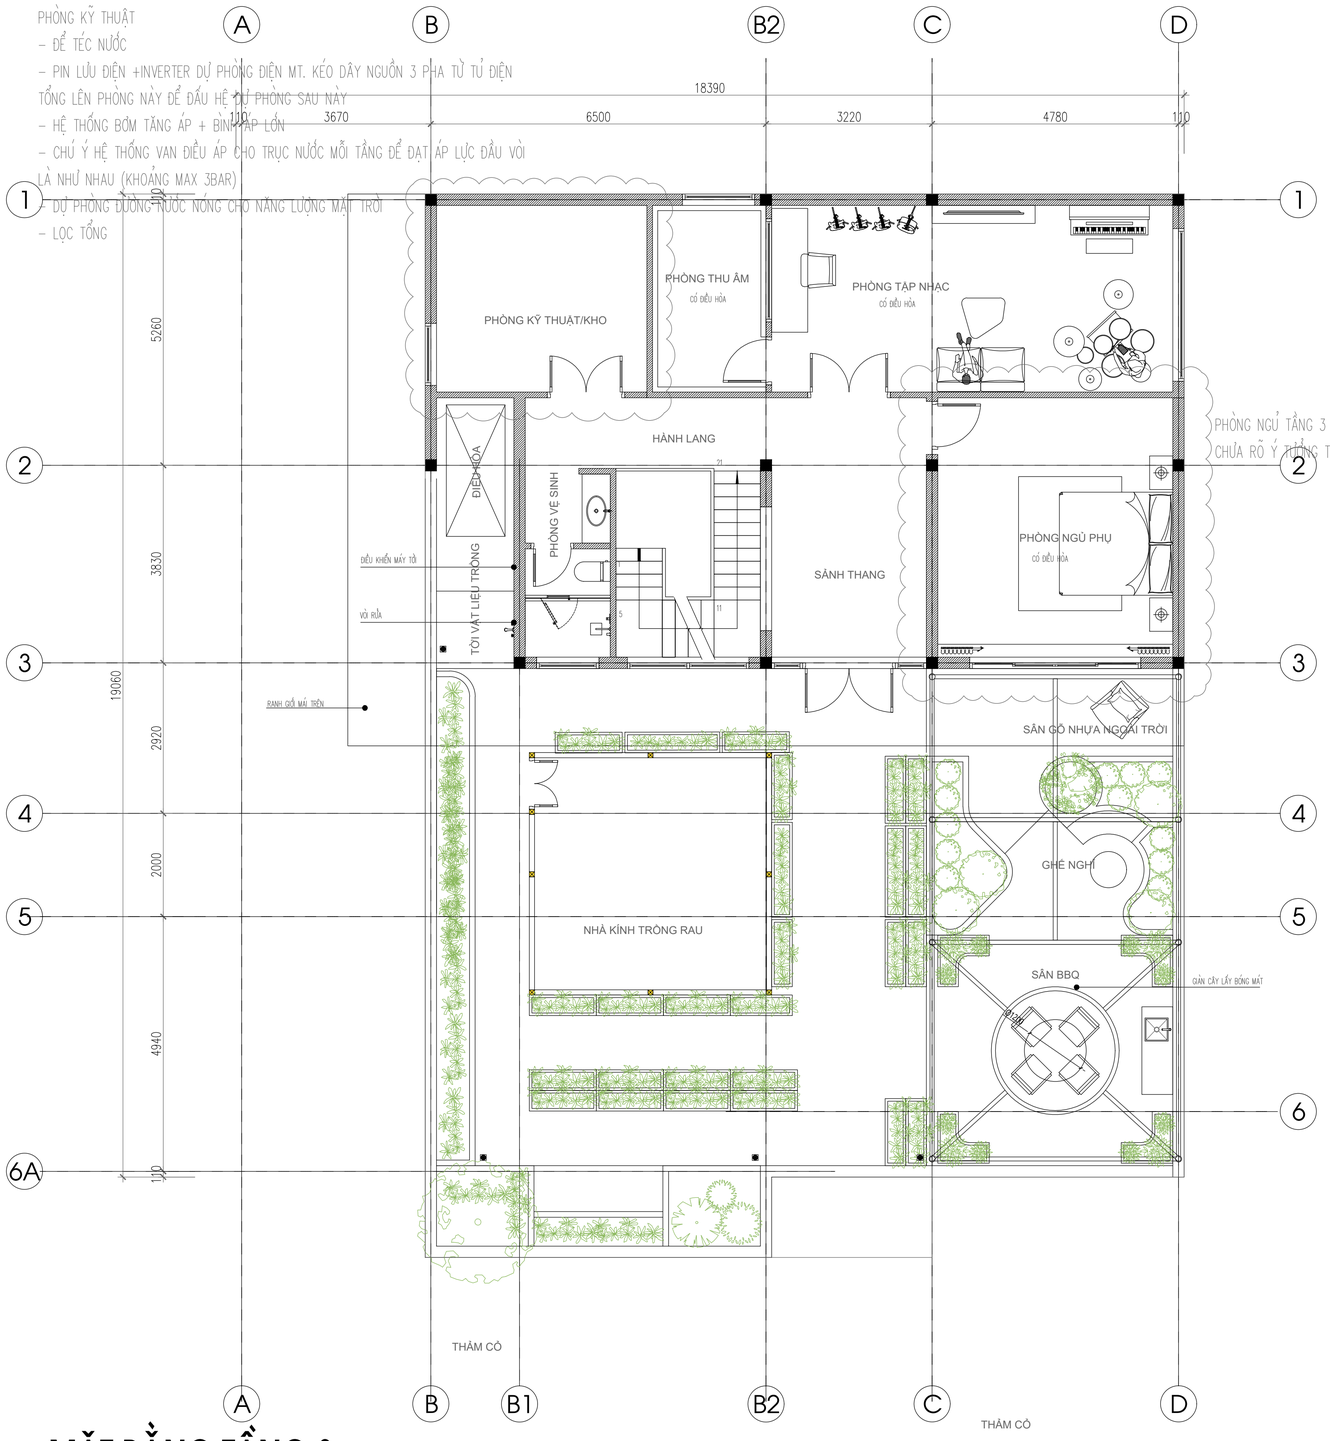

MẶT BẰNG TẦNG 3

MB
...

1:100

A. NGUYÊN LÝ CẤP NƯỚC

– 1 TRỤC ĐI THẲNG TỪ NGUỒN CẤP LÊN TÉC CHỮA SỐ 1 –> LỌC TỔNG –> TÉC CHỮA 2

– 1 TRỤC CẤP VÀO BỂ TRỮ NƯỚC TẦNG 1

– NƯỚC QUA BỂ TRỮ CẦN QUA 1 HỆ THỐNG LỌC THÔ

– NƯỚC MƯA GOM VỀ AO HƯỚNG ĐÔNG

B. CẤP ĐIỆN

– CẤP ĐIỆN CHO KHỐI NHÀ ĂN VÀ NHÀ THỜ DỰ PHÒNG, LẤY TỪ NGUỒN CẤP TỦ TỔNG NHÀ CHÍNH

– Ổ CẮM ĐIỆN Ở CÁC KHÔNG GIAN KHÔNG CHỈ ĐỊNH THÌ BỐ TRÍ CƠ BẢN VÌ NHU CẦU KHÔNG QUÁ NHIỀU, NHƯNG VẪN CẦN MỖI KHÔNG GIAN ÍT NHẤT 1 2 Ổ ĐIỆN Ở VỊ TRÍ THUẬN TIỆN

–RCBO CHO CÁC THIẾT BỊ NHƯ BÌNH NÓNG LẠNH, Ổ CẮM LÀ BẮT BUỘC

– THÔNG GIÓ CẤP KHÍ TƯƠI CHO PHÒNG NGỦ + PHÒNG LÀM VIỆC CHÍNH (CÂN NHẮC CẤP KHÍ TƯƠI TUẦN HOÀN NHIỆT DAIKIN + HỆ ĐIỀU HÒA)

– LƯU Ý HỆ THỐNG ĐIỆN DỰ PHÒNG: CẤP DỰ PHÒNG CHO WIFI, ÁNH SÁNG DỰ PHÒNG, DỰ PHÒNG CHO PHÒNG NGỦ MASTER + LÀM VIỆC TẦNG 2 LÀ CHÍNH

C. CHIẾU SÁNG

– THIÊN VỀ ÁNH SÁNG SPOT, CÓ CHIỀU SÂU VÀ PHÂN LỚP

– CÁC KHÔNG GIAN TÁC VỤ NHƯ: BẾP CẦN SÁNG. VỆ SINH DÙNG SPOT + ĐÈN HẮT ÁNH SÁNG GIÁN TIẾP

– 1 SỐ GÓC LUÔN BẬT ĐÈN: SẢNH PHÒNG KHÁCH, SẢNH GIỮA NHÀ TẦNG 2

– CHIẾU SÁNG NGOẠI CẢNH: ÁNH SÁNG DẪN HƯỚNG VÀ KHÔNG CHÓI MẮT

– 2 CÂY TRƯỚC CỬA PHÒNG LÀM VIỆC CẦN CHIẾU SÁNG ĐỂ NUÔI CÂY

GHI CHÚ
Toàn bộ kích thước trong hồ sơ là kích thước hoàn thiện.
Kiểm tra lại kích thước thực tế trước khi thi công.
Kết hợp các bản vẽ kiến trúc, kết cấu, điện, nước để thi công.
Phải thực hiện đầy đủ những chỉ dẫn kỹ thuật trong bản vẽ.
Không thay đổi bản vẽ dưới mọi hình thức nếu không được sự chấp thuận của đơn vị thiết kế.
© COPYRIGHT 2016

NGÀY	LẦN	NỘI DUNG SỬA ĐỔI
.../.../...	1	
.../.../...	2	
.../.../...	3	

DỰ ÁN :
.....
ĐỊA ĐIỂM: .....
.....

CHỦ ĐẦU TƯ :
.....
ĐỊA CHỈ : .....
.....
TEL: .....

I.D ARCHITECTURE AND FURNITURE
ĐỊA CHỈ: SỐ 74A/116 NHÂN HÒA, NHÂN CHÍNH, HÀ NỘI
TEL: 04 22 84 66 99
WEBSITE: HTTP://IDSTUDIO.VN

CHỦ TRÌ DỰ ÁN	THIẾT KẾ CHÍNH	NGƯỜI VẼ	KIỂM

TÊN BẢN VẼ
PHƯƠNG ÁN SƠ BỘ

NGÀY:.....
TỶ LỆ: 1/100
HIỆU CHỈNH 00
BẢN VẼ KT-